


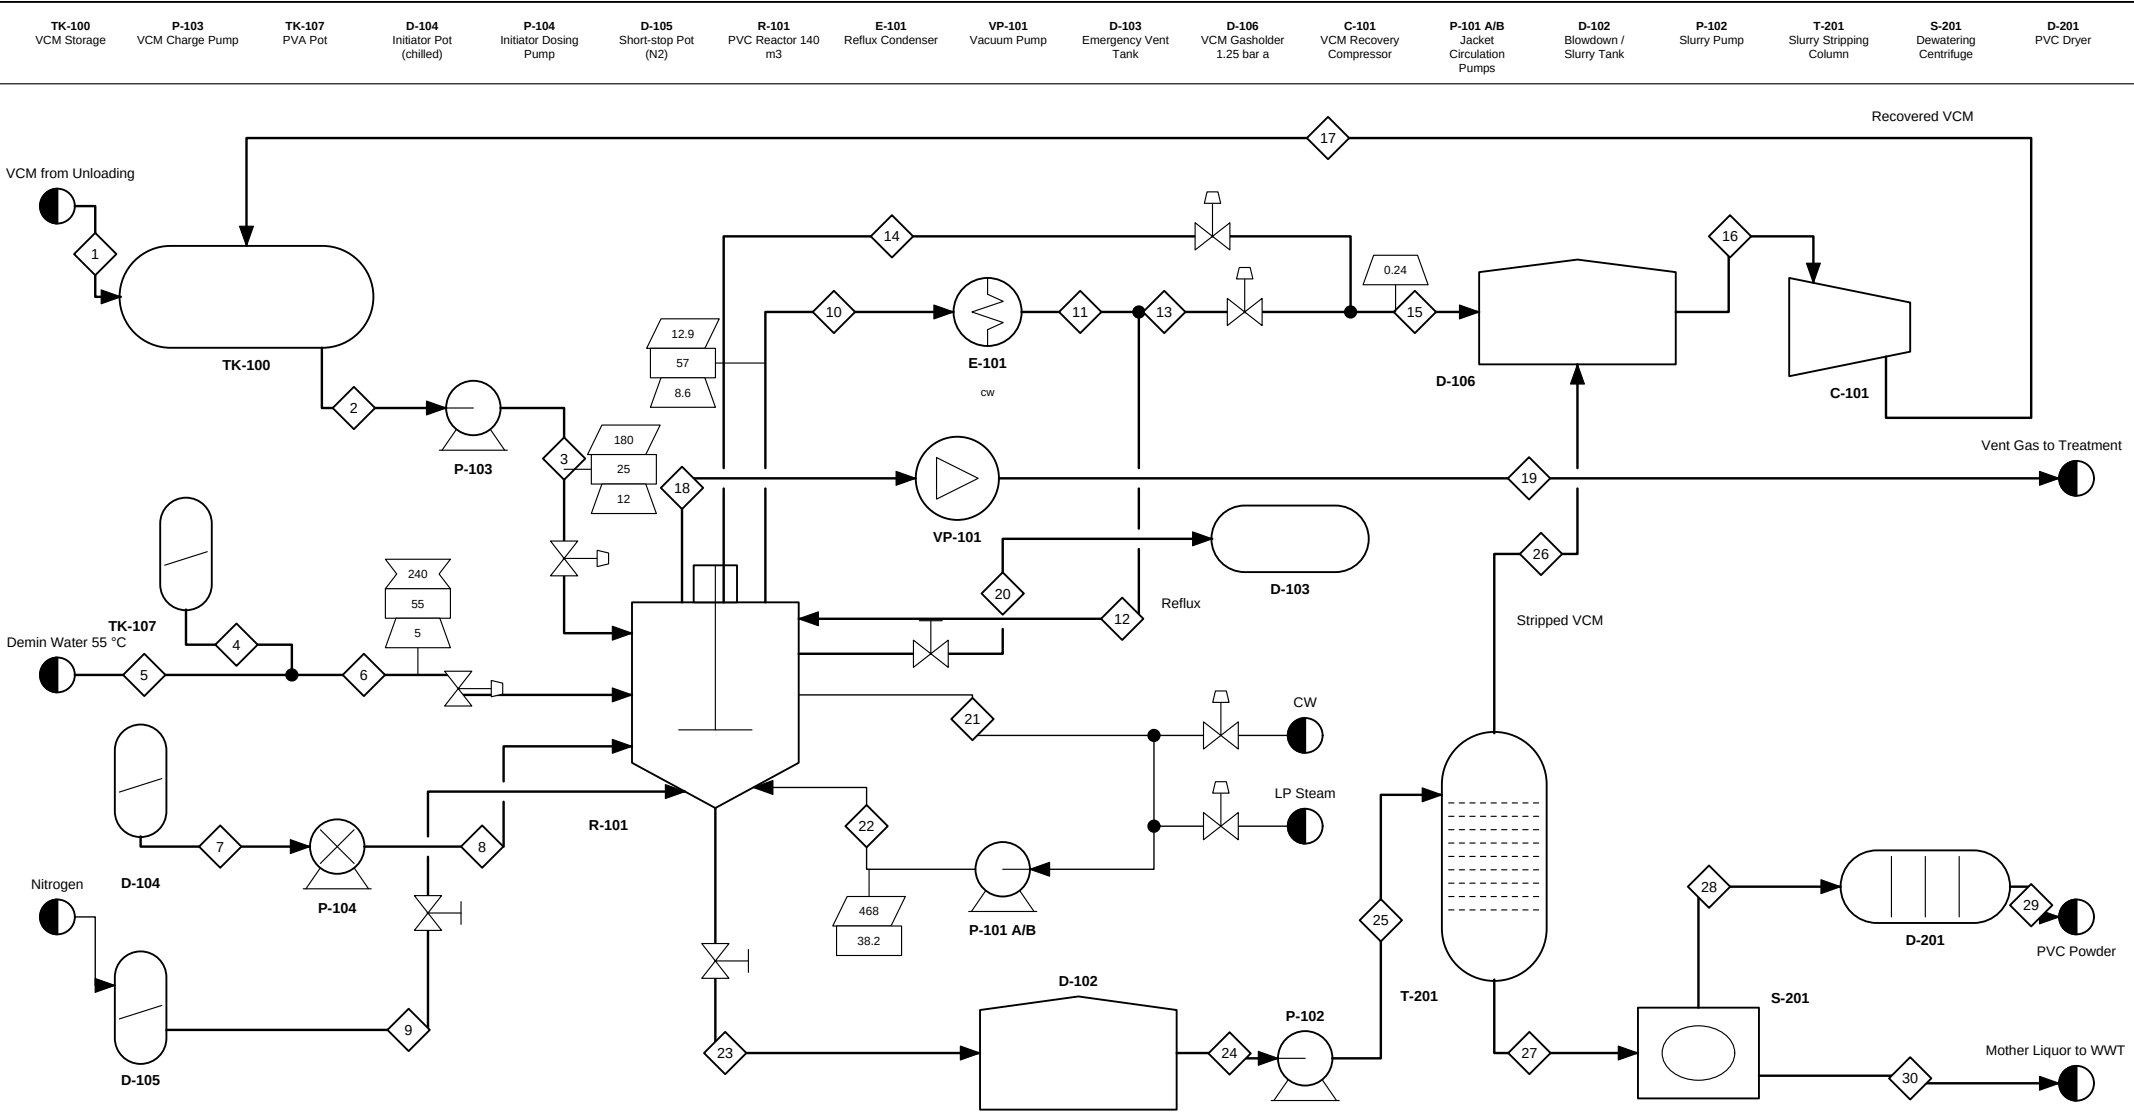

NOTES

1. Flags: R-101 design state 2.0 h into the reaction (OTS model); charge rates are the FIC set points.

2. Batch: 60 t water + PVA, 51 t VCM, initiator; 57 °C, 8.6 bar g; end point at 1.8 bar pressure drop.

3. Recovered VCM is condensed before storage (condenser not shown). Baffle CW and N2 pad not shown.

4. T-201, S-201, D-201 are shared by R-101 to R-104 and shown as blocks only.

LEGEND

Mass Flow (t/h)	Liquid Flow (m³/h)	Temperature (°C)	Pressure (bar g)	Process Line	Utility Line
Block Valve	Control Valve	Process Input / Output	Stream Number	Line Crossing	Vessel / Drum
Centrifugal Pump	PD Pump	Stirred Reactor	Heat Exchanger	Blower / Fan	Storage Tank

PVC SUSPENSION REACTOR VER 1 - OPERATOR TRAINING SIMULATOR			
PFD-100 PVC suspension polymerisation — R-101 area			
PVC SUSPENSION POLYMERISATION — R-101 AREA (1 OF 4 REACTORS)			
DRAWING No. PFD-100	REV. 0	SIZE A4	SHEET 1 OF 1
DRAWN Apinan Soottitantawat	CHECKED	SCALE NTS	DATE 2026-09-29