
TK-101
BFW Storage Tank

P-101 A/B
BFW Pumps

E-101
BFW Heater (steam in shell)

Y-101
Condensate Strainer

ST-101
Steam Trap

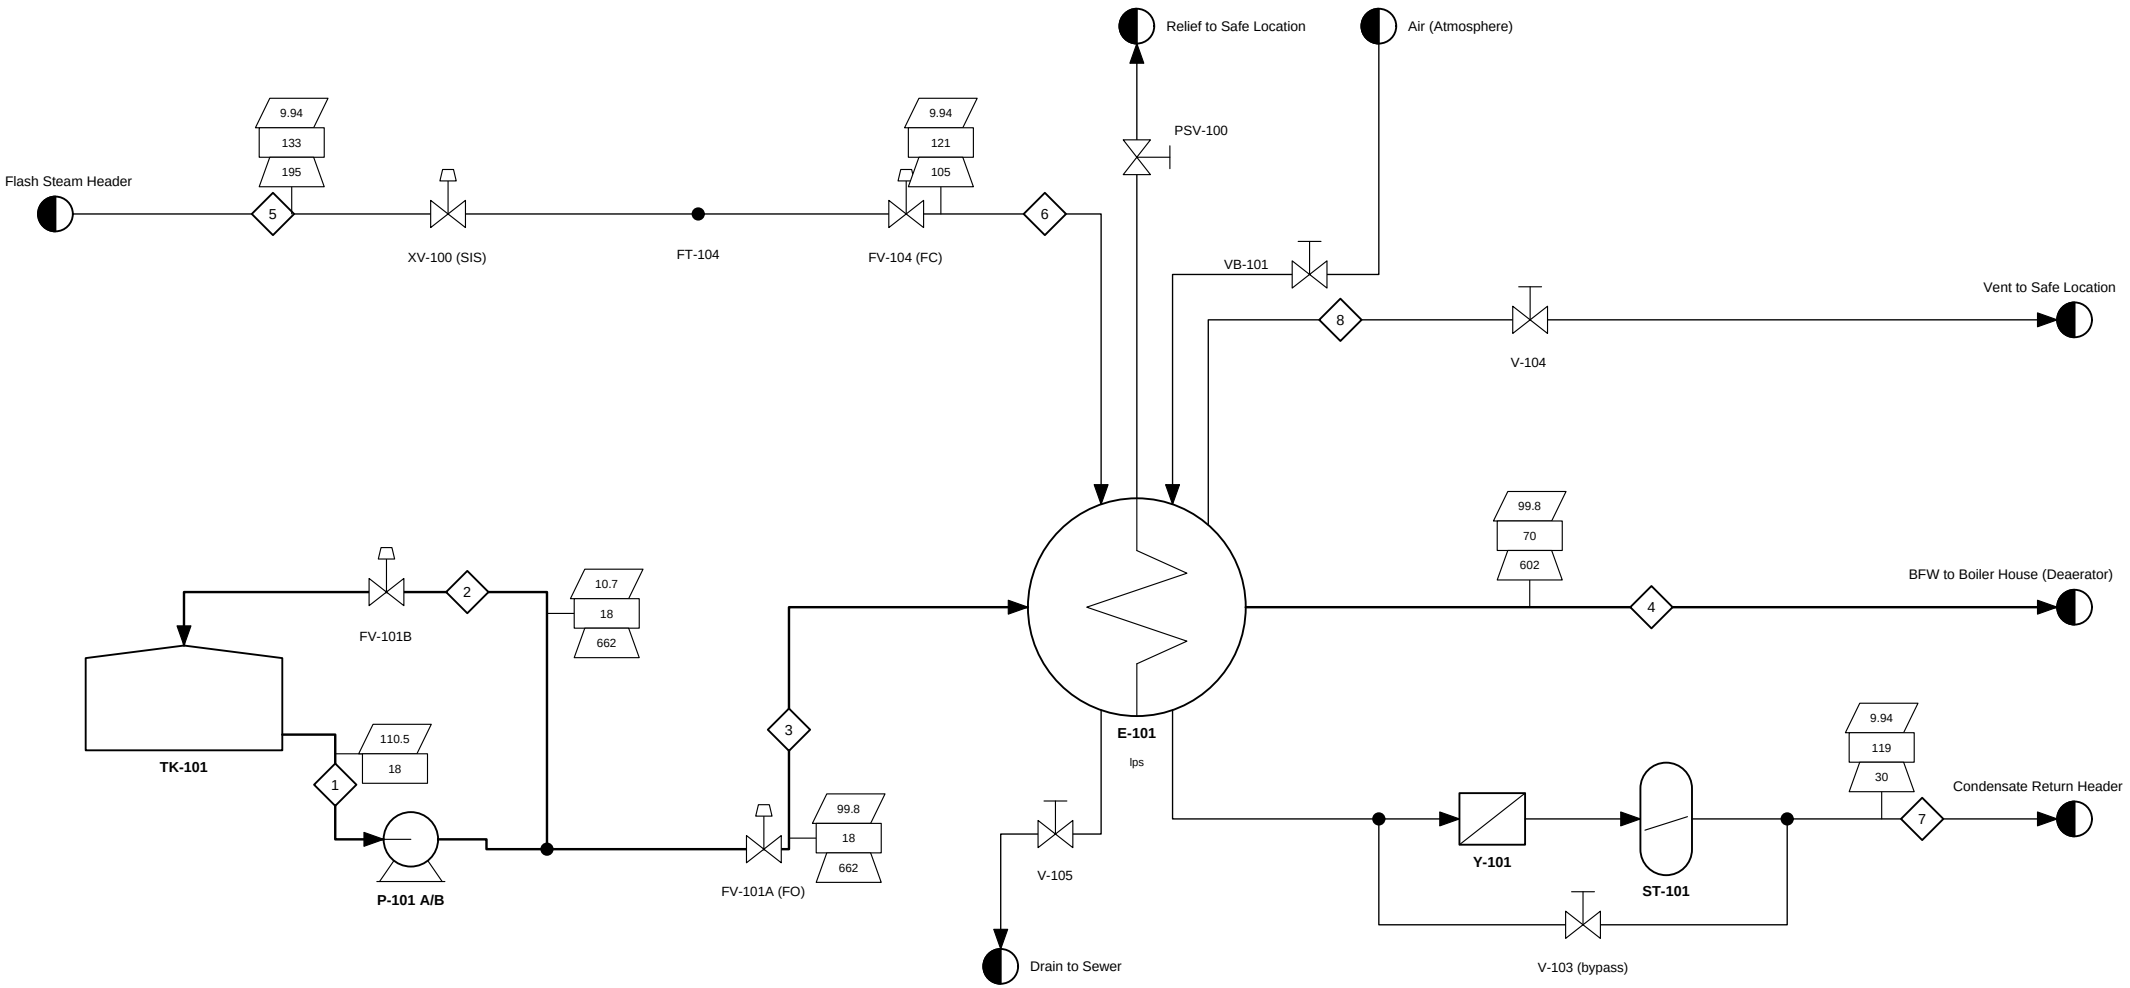

NOTES

1. Flows in 1000 kg/h; temperatures in °C; pressures in kPa g. Design point of the simulator model.
2. Stream 8: vent V-104, trap bypass V-103 and shell drain V-105, all closed at design (no flags).
3. XV-100 is the SIS steam shut-off (FSLL-101, TSHH-108, PSHH-100, ESD).

LEGEND

- Mass Flow (1000 kg/h)
- Temperature (°C)
- Pressure (kPa g)
- Process Line
- Utility Line
- Block Valve
- Control Valve
- Process Input / Output
- Stream Number
- Line Crossing
- Storage Tank
- Centrifugal Pump
- Heat Exchanger
- Filter
- Vessel / Drum

BFW STEAM HEATER VER 1 - OPERATOR TRAINING SIMULATOR

PROCESS FLOW DIAGRAM

BFW STEAM HEATER E-101 - FLASH-STEAM BFW HEATING

DRAWING No.	REV.	SIZE	SHEET
BFW-PFD-100	0	A4	1 OF 1
DRAWN	**CHECKED**	**SCALE**	**DATE**
Apinan Soottitantawat		NTS	2026-09-29