


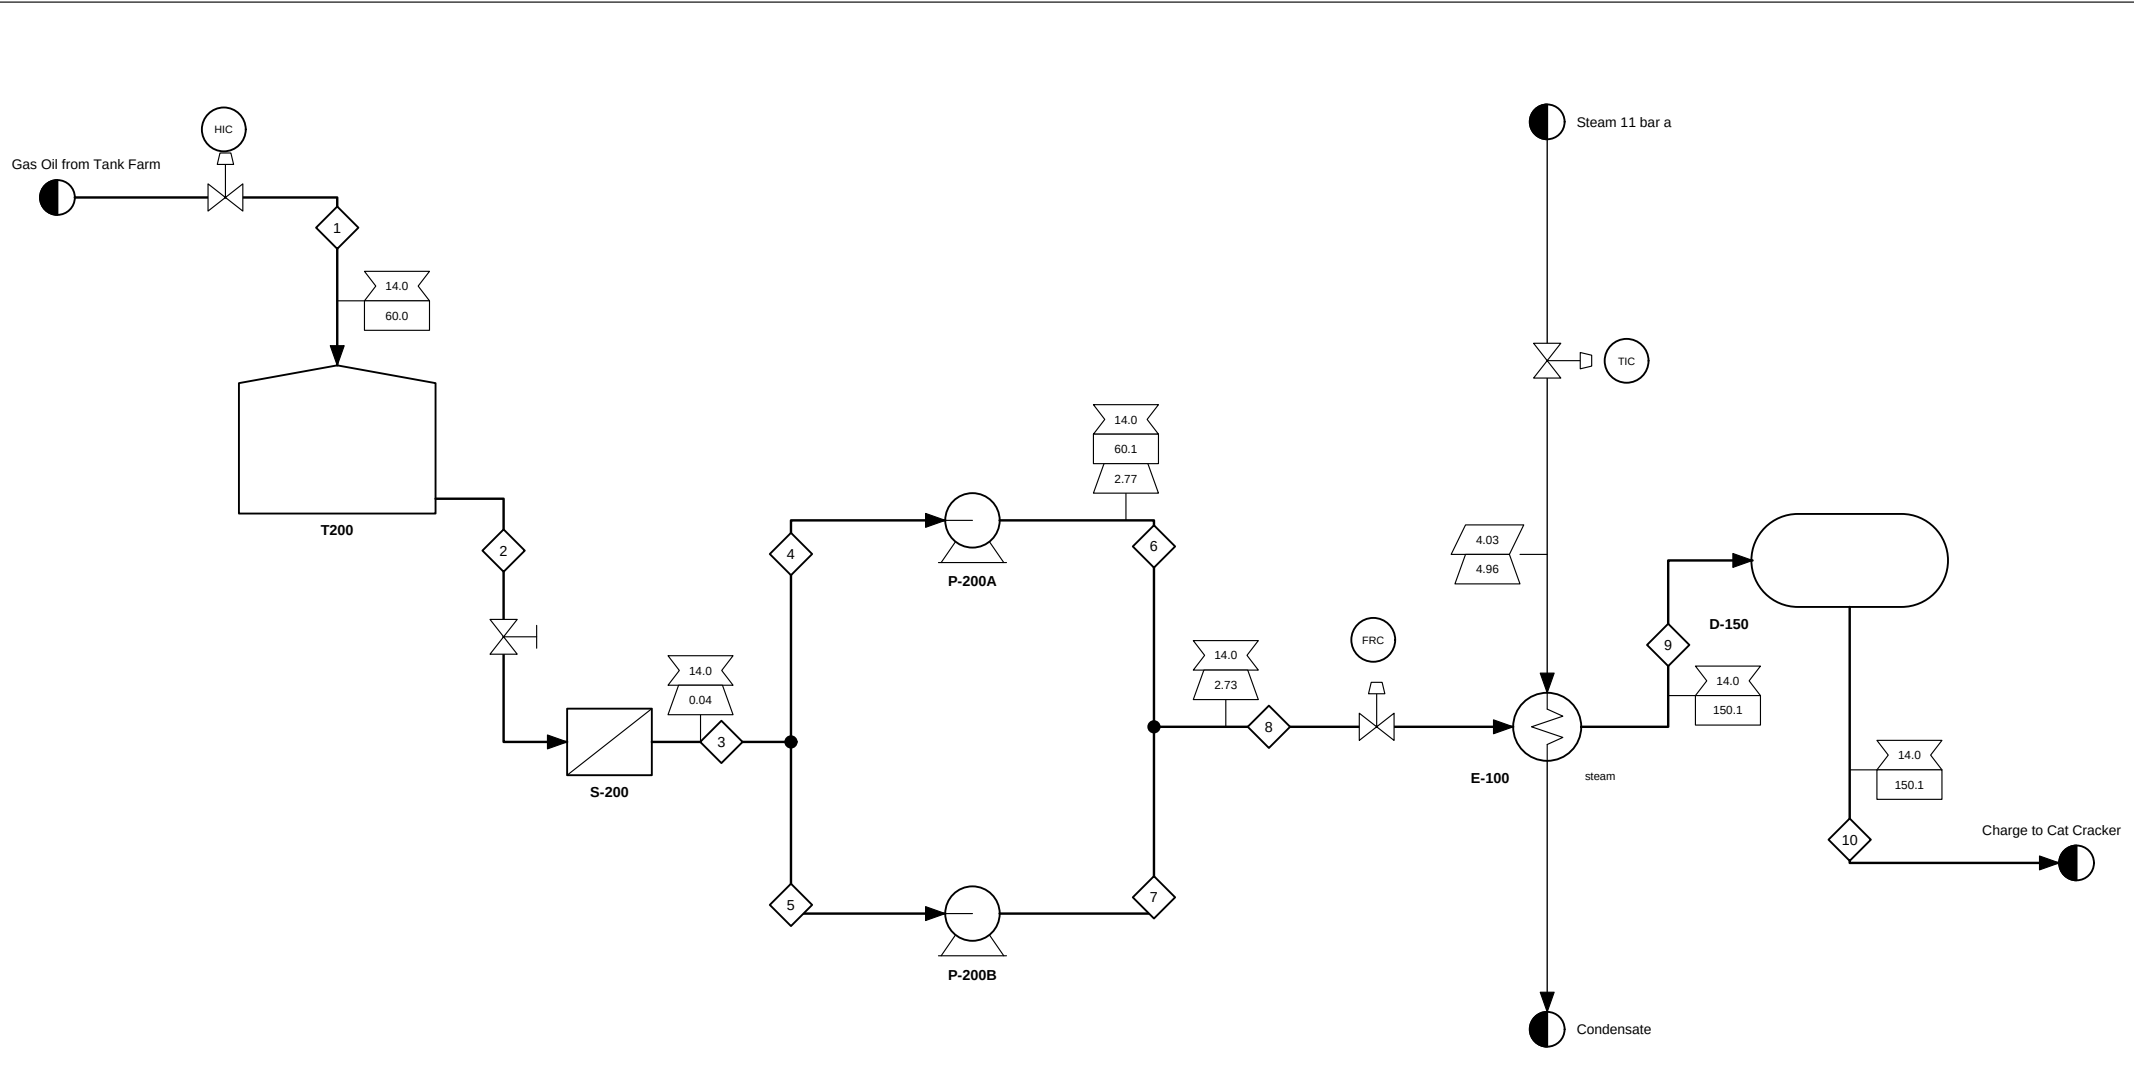

NOTES

1. Flags: OTS design state — P-200A running, P-200B spare lined up (idle), FRC-100 AUTO 14 L/s, TIC-110 MAN 50 %.

2. Gas oil 870 kg/m3, 60 °C in T200. Pressures in bar g from the model heads (m of liquid); steam in bar g in the E-100 shell.

3. Suction and discharge block valves, check valves NRV-210/220, local gauges, drains, vents and trips: see P&ID PPS-PID-001.

4. Sizes: T200 Ø12 x 10 m, D-150 30 m3 (model); other symbols indicative.

LEGEND

Liquid Flow (L/s)

Mass Flow (t/h)

Temperature (°C)

Pressure (bar g)

Process Line

Utility Line

Block Valve

Control Valve

Process Input / Output

Stream Number

Line Crossing

Storage Tank

Filter

Centrifugal Pump

Heat Exchanger

Vessel / Drum

PARALLEL PUMP STATION VER 1 · OPERATOR TRAINING SIMULATOR			
PROCESS FLOW DIAGRAM			
PARALLEL PUMP STATION — CAT-CRACKER FEED, T200 TO D-150			
DRAWING No. PPS-PFD-100	REV. 0	SIZE A4	SHEET 1 OF 1
DRAWN Apinan Soottitantawat	CHECKED	SCALE NTS	DATE 2026-10-08