**V-101** Inlet Scrubber | **K-100 S1** Export Compressor Section 1 (LP) | **E-101** Intercooler | **V-102** Interstage Scrubber | **K-100 S2** Export Compressor Section 2 (HP) | **E-102** Aftercooler | **GT-100** Gas Turbine Driver (22 MW ISO) | **V-900** Flare KO Drum (PID-900) | **P-160** Cooling Medium Pump

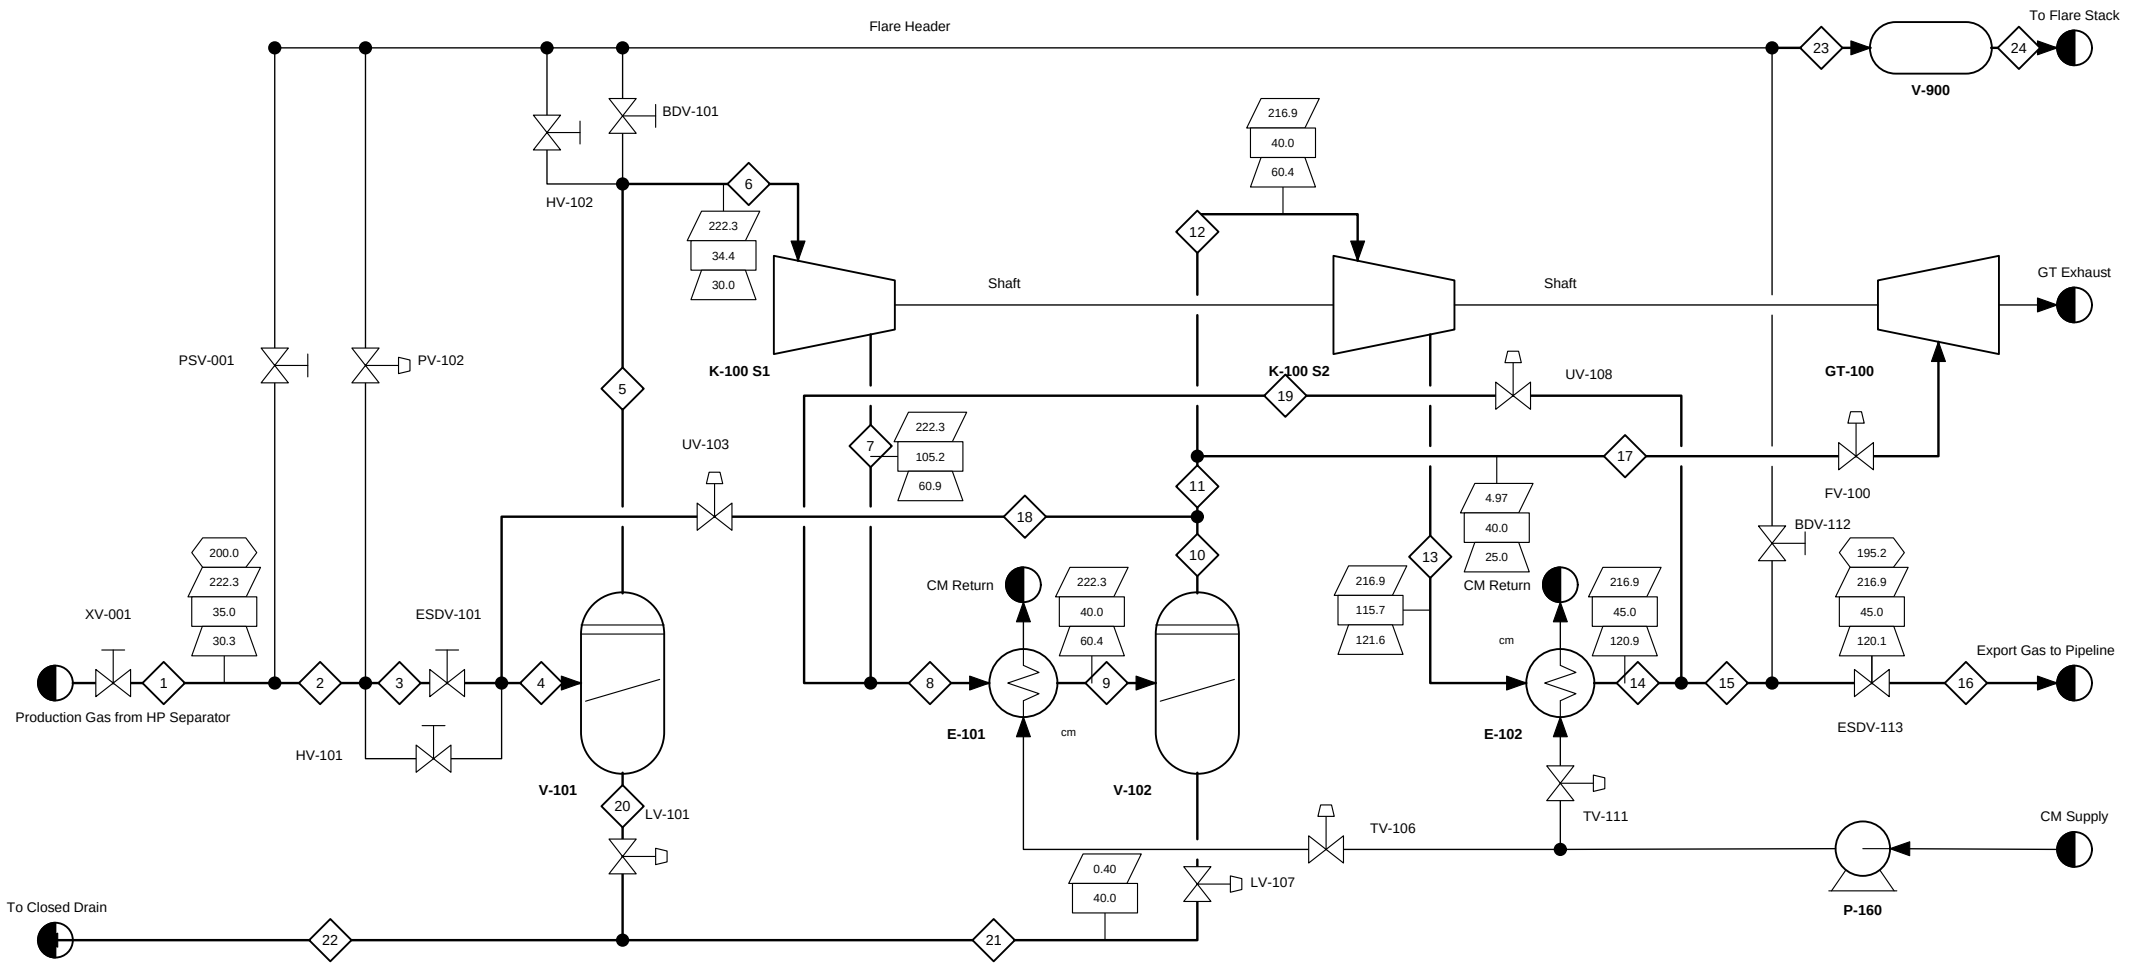


**NOTES**

1. Flags: OTS design state (200 MMSCFD, PIC-101 30.0 barg → SIC-100 speed; UV-103, UV-108, PV-102 shut). Pressures in barg.
2. K-100 sections 1 and 2: one casing, one shaft, direct drive by GT-100. UV-103/UV-108 recycle cooled gas (anti-surge).
3. Relief, blowdown, vent and bypass lines (PSV-001, PV-102, BDV-101/112, HV-101/102) drawn light. Trips and line sizes: P&ID KC-PID-100.
4. Symbol sizes indicative. Flare KO drum and stack on PID-900 (tag V-900 assumed). Fuel-gas skid and seawater CM cooler not shown.

**LEGEND**

Gas Flow (MMSCFD) · Mass Flow (t/h) · Temperature (°C) · Pressure (barg) · Process Line · Utility Line

Block Valve · Control Valve · Process Input / Output · Stream Number · Line Crossing · Separator

Compressor · Heat Exchanger · Turbine / Expander · Vessel / Drum · Centrifugal Pump

GAS EXPORT COMPRESSOR VER 1 · OPERATOR TRAINING SIMULATOR

## PROCESS FLOW DIAGRAM

GAS EXPORT COMPRESSOR K-100 — TWO SECTIONS, GT-100 DRIVER

| DRAWING No. | REV. | SIZE | SHEET |
|---|---|---|---|
| KC-PFD-100 | A | A4 | 1 OF 1 |
| **DRAWN** | **CHECKED** | **SCALE** | **DATE** |
| Apinan Soottitantawat | | NTS | 2026-10-11 |